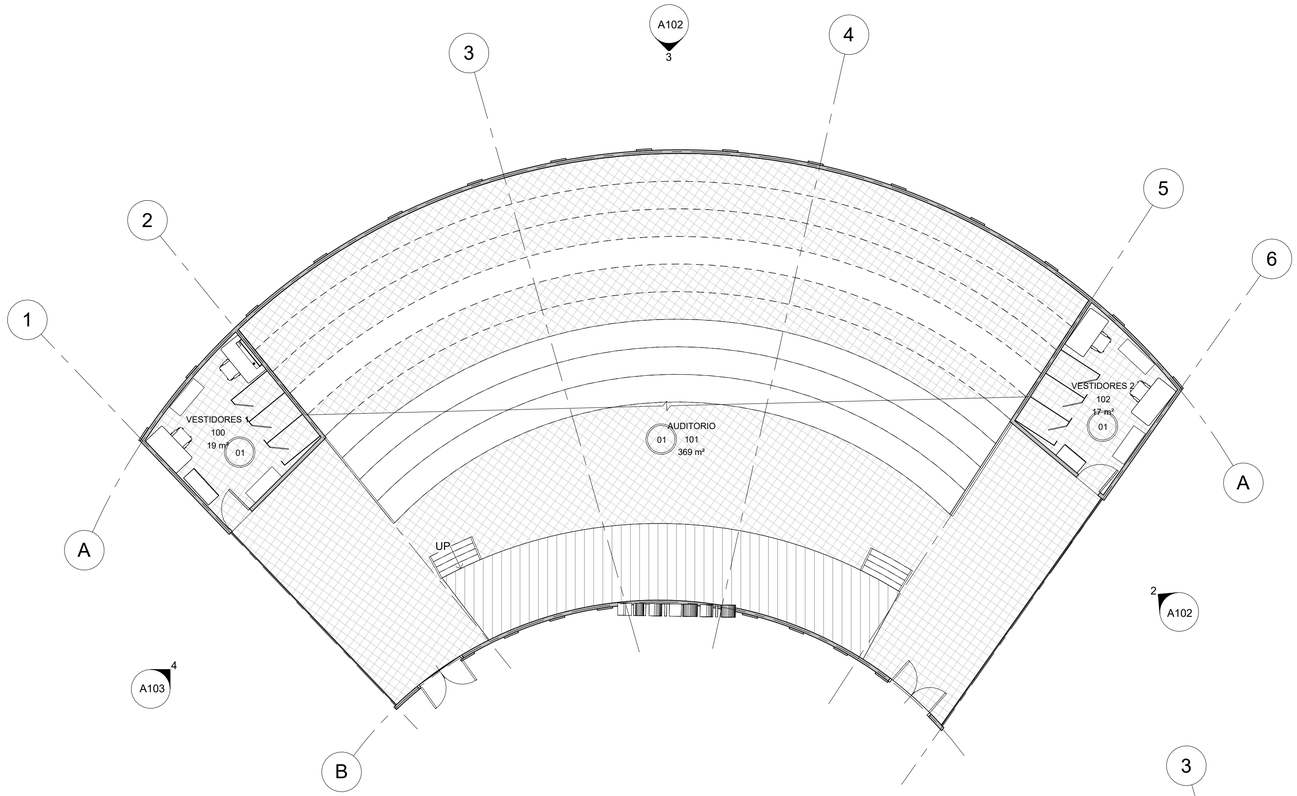

1 02.PLANTA ACABADOS

1 : 100

TABLA DE PISO	
Model	Description
01	PISO DE CERÁMICA ANTIDERRAPANTE COLOR CLARO

CUADRO DE CIELOS			
Number	Model	Perimeter	Area
100	01	84.69	371 m²
101	01	17.28	20 m²
102	01	16.57	18 m²

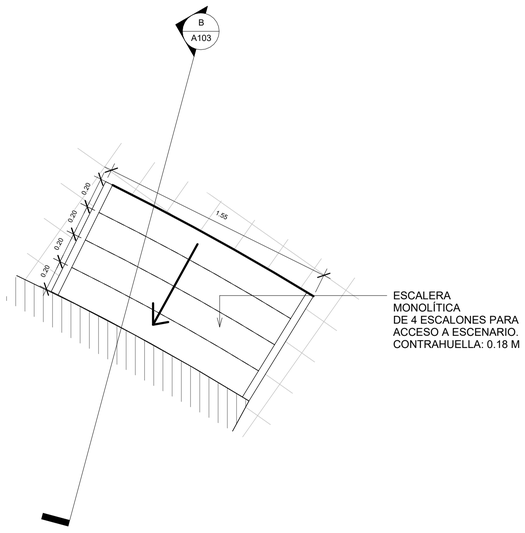

ESCALERA
MONOLÍTICA
DE 4 ESCALONES PARA
ACCESO A ESCENARIO.
CONTRAHUELLA: 0.18 M

3 DETALLE DE ESCALERA

1 : 20

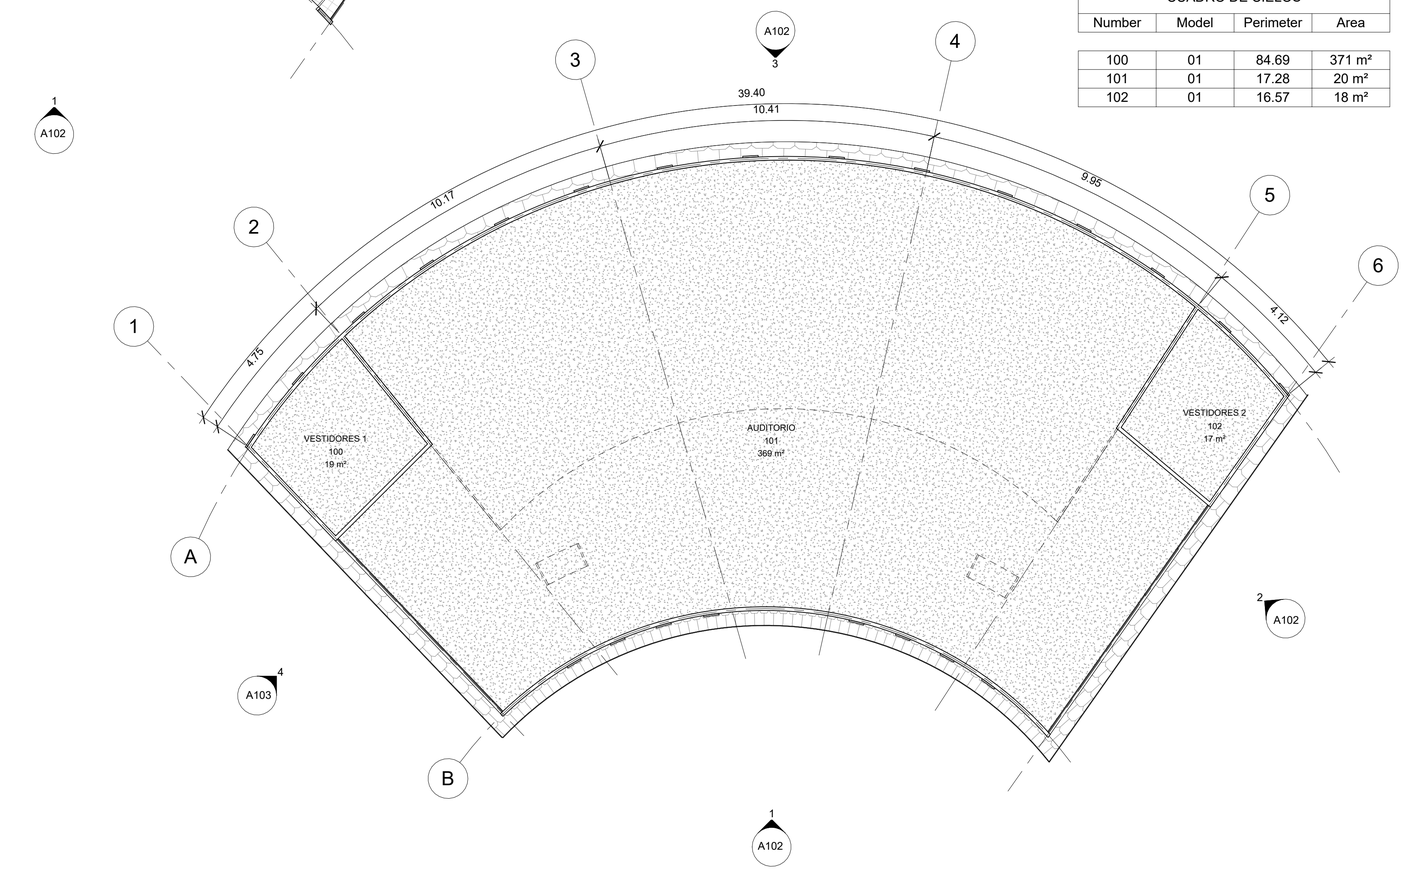

2 PLANTA DE CIELO

1 : 100

ARQ. ORELIO MARTINEZ
ARCHITECTURAL ADVISORY SERVICES

No.	Description	Date

ST Helen's American Academy Bilingual School

Project Name

PLANTAS DE ACABADO

Project number	0001
Date	Issue Date
Drawn by	ARQ.MARÍA LAURA ESPINOZA
Checked by	ARQ.ING.ORELIO MARTÍNEZ

A105

Scale: As indicated

5/14/2024 12:45:11 PM