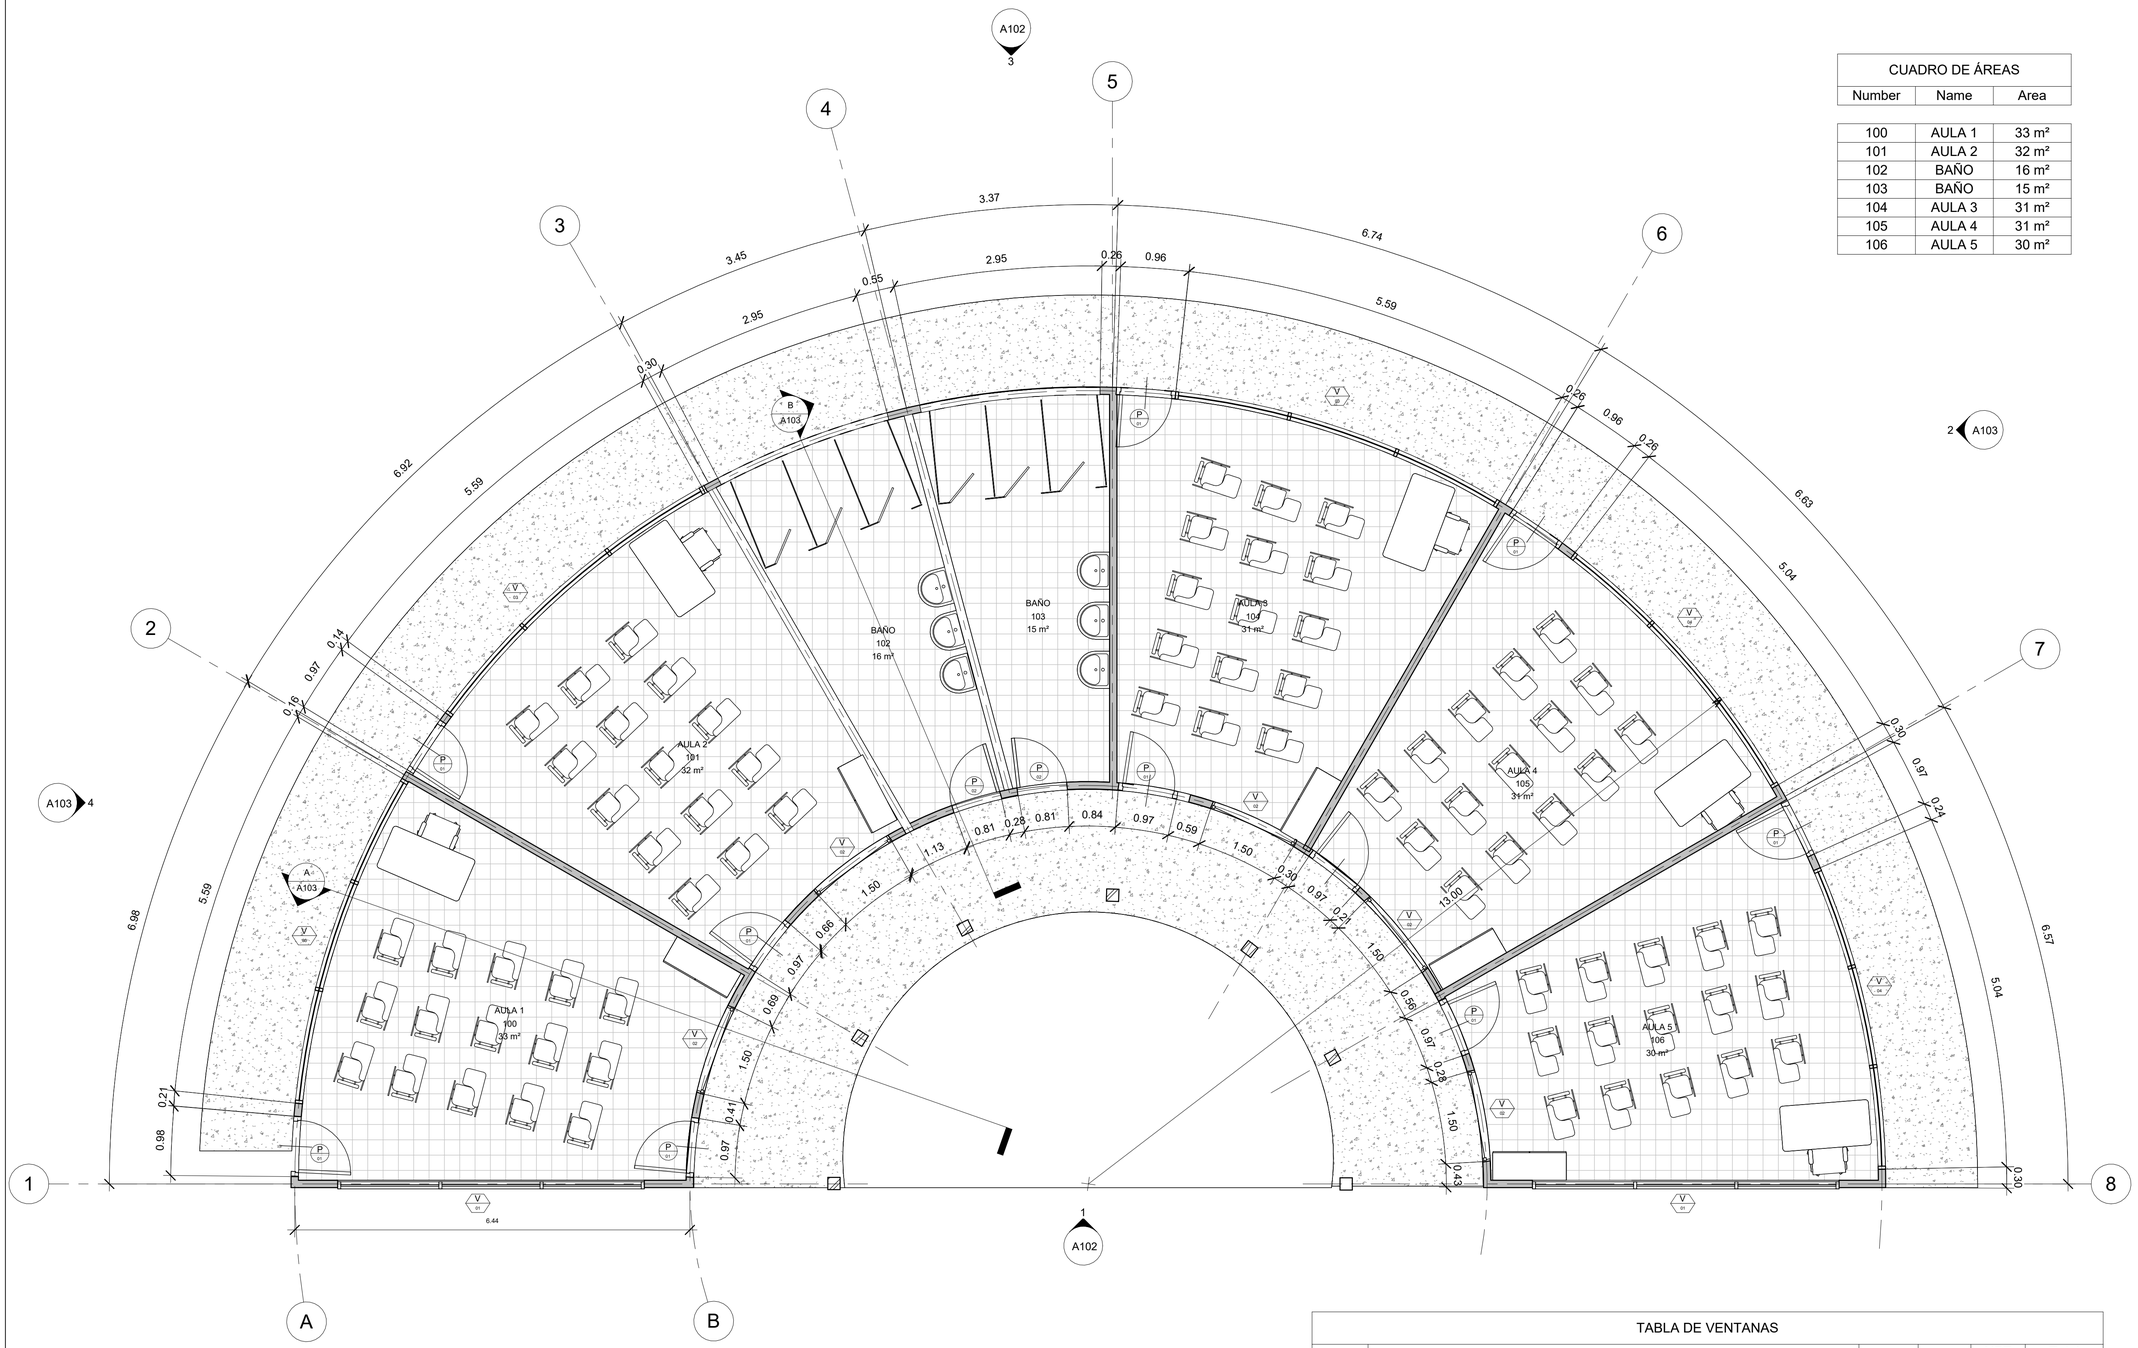

1 01.PLANTA ARQ

1 : 50

CUADRO DE ÁREAS		
Number	Name	Area
100	AULA 1	33 m²
101	AULA 2	32 m²
102	BAÑO	16 m²
103	BAÑO	15 m²
104	AULA 3	31 m²
105	AULA 4	31 m²
106	AULA 5	30 m²

TABLA DE PUERTAS				
Model	Height	Width	Description	Total doors
01	2.08	0.85	PUERTA DE UNA HOJA ABATIBLE CON MARCO Y HOJA METÁLICA Y VENTANA	10
02	2.10	0.81	PUERTA DE UNA HOJA ABATIBLE CON MARCO Y HOJA DE MADERA	2

TABLA DE VENTANAS					
Model	Description	Width	Height	NPT height	Total windows
01	VENTANA ABATIBLE DE DOS CUERPOS CON MARCO DE ALUMINIO Y VIDRIO TEMPLADO DE 6 MM TRANSPARENTE	5.00	1.20	1.00	2
02	VENTANA ABATIBLE DE DOS CUERPOS CON MARCO DE ALUMINIO Y VIDRIO TEMPLADO DE 6 MM TRANSPARENTE	1.50	1.10	1.00	5
03	VENTANA ABATIBLE DE DOS CUERPOS CON MARCO DE ALUMINIO Y VIDRIO TEMPLADO DE 6 MM TRANSPARENTE	5.59	1.20	1.00	3
04	VENTANA ABATIBLE DE DOS CUERPOS CON MARCO DE ALUMINIO Y VIDRIO TEMPLADO DE 6 MM TRANSPARENTE	5.04	1.20	1.00	2
05	VENTANA ABATIBLE DE DOS CUERPOS CON MARCO DE ALUMINIO Y VIDRIO TEMPLADO DE 6 MM TRANSPARENTE	0.48	2.95	1.85	2

ARQ. ORELIO MARTINEZ
ARCHITECTURAL ADVISORY SERVICES

No.	Description	Date

ST Helen's American Academy Bilingual School

Project Name

PLANTA ARQ EDIFICIO S

Project number	0001
Date	Issue Date
Drawn by	Arq. María Laura Espinoza
Checked by	ARQ.ING. ORELIO MARTÍNEZ

A101

Scale 1 : 50

5/14/2024 12:46:11 PM