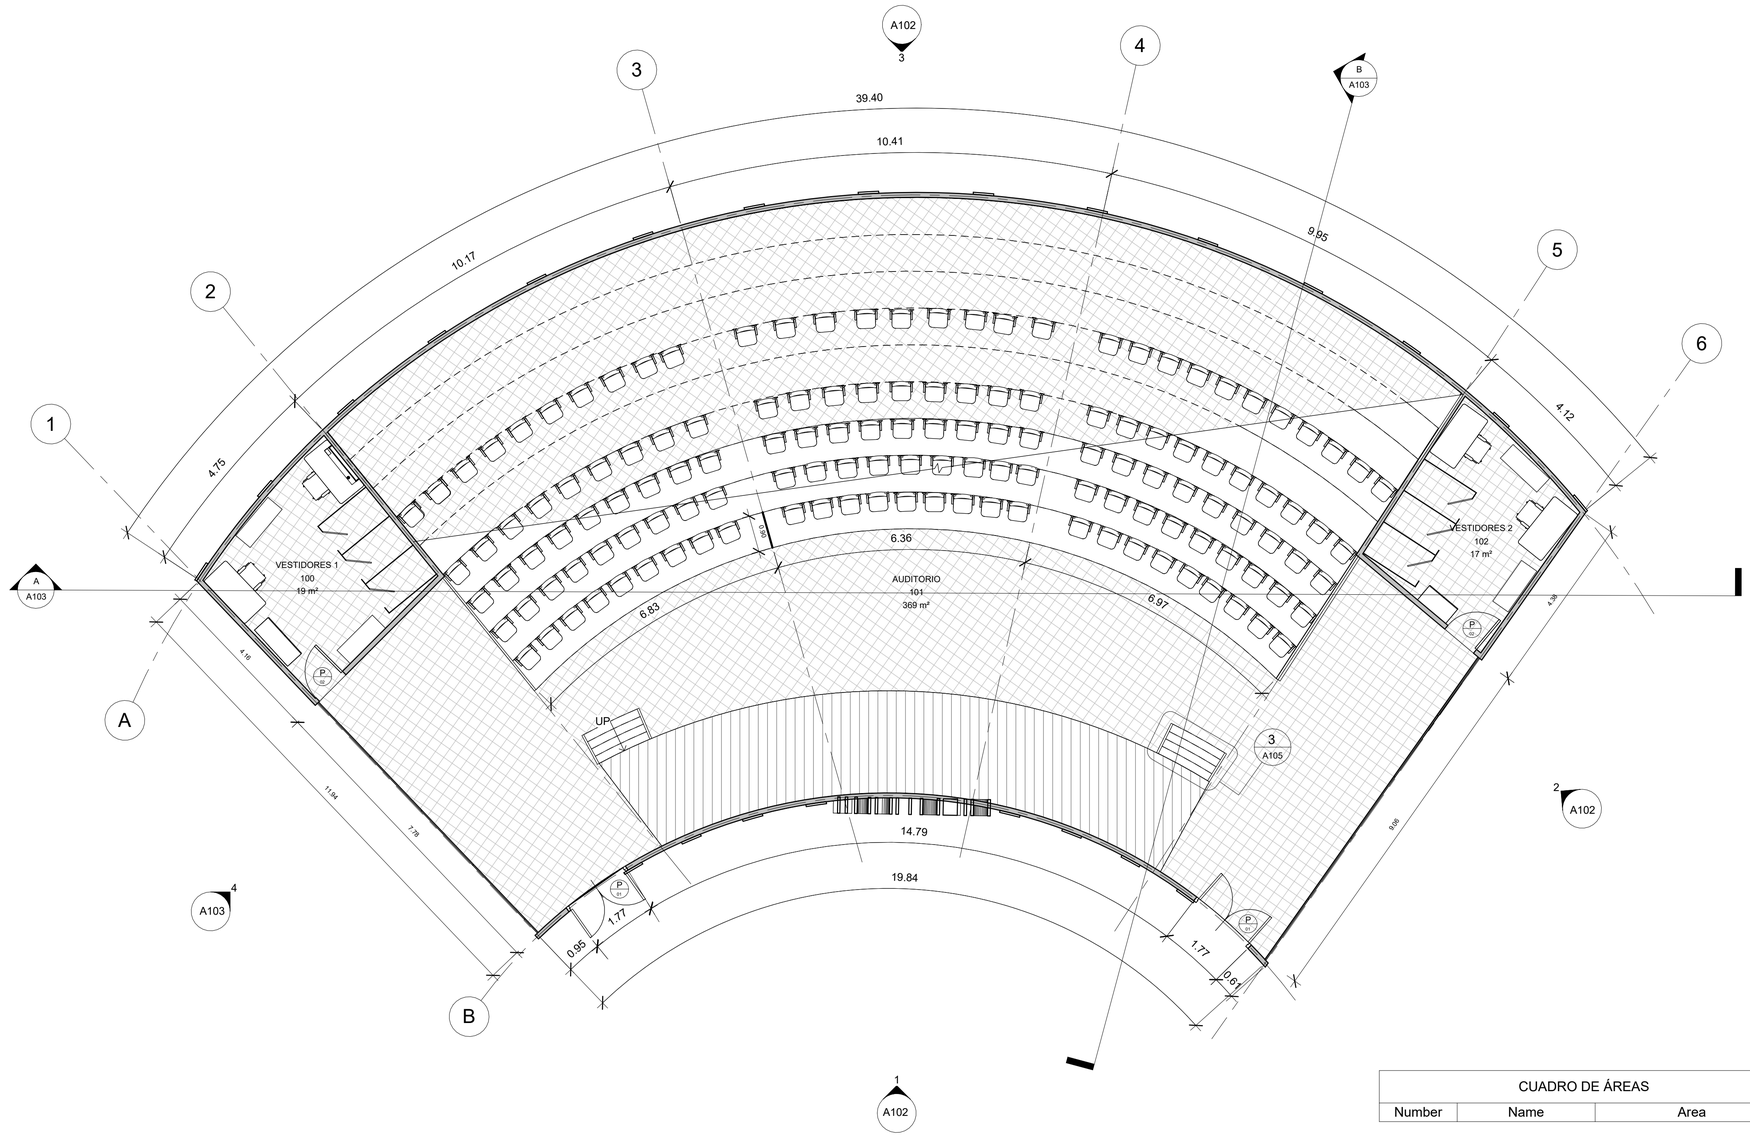


1 01.PLANTA ARQ

1 : 75

CUADRO DE ÁREAS		
Number	Name	Area
100	VESTIDORES 1	19 m²
101	AUDITORIO	369 m²
102	VESTIDORES 2	17 m²

TABLA DE PUERTAS				
Model	Width	Height	Description	Total Doors
01	1.65	2.08	PUERTA DOBLE HOJA ABATIBLE DE VIDRIO DE 8 MM CON MARCO DE ALUMINIO	2
02	0.92	2.13	PUERTA CON MARCO Y HOJA DE MADERA ABATIBLE	2

ARQ. ORELIO MARTINEZ
ARCHITECTURAL ADVISORY SERVICES

No.	Description	Date

ST Helen's American Academy Bilingual School

Project Name

PLANTA ARQ AUDITORIO

Project number	0001
Date	Issue Date
Drawn by	Arq. María Laura Espinoza
Checked by	ARQ.ING. ORELIO MARTÍNEZ

A101

Scale 1 : 75

5/14/2024 12:41:39 PM